
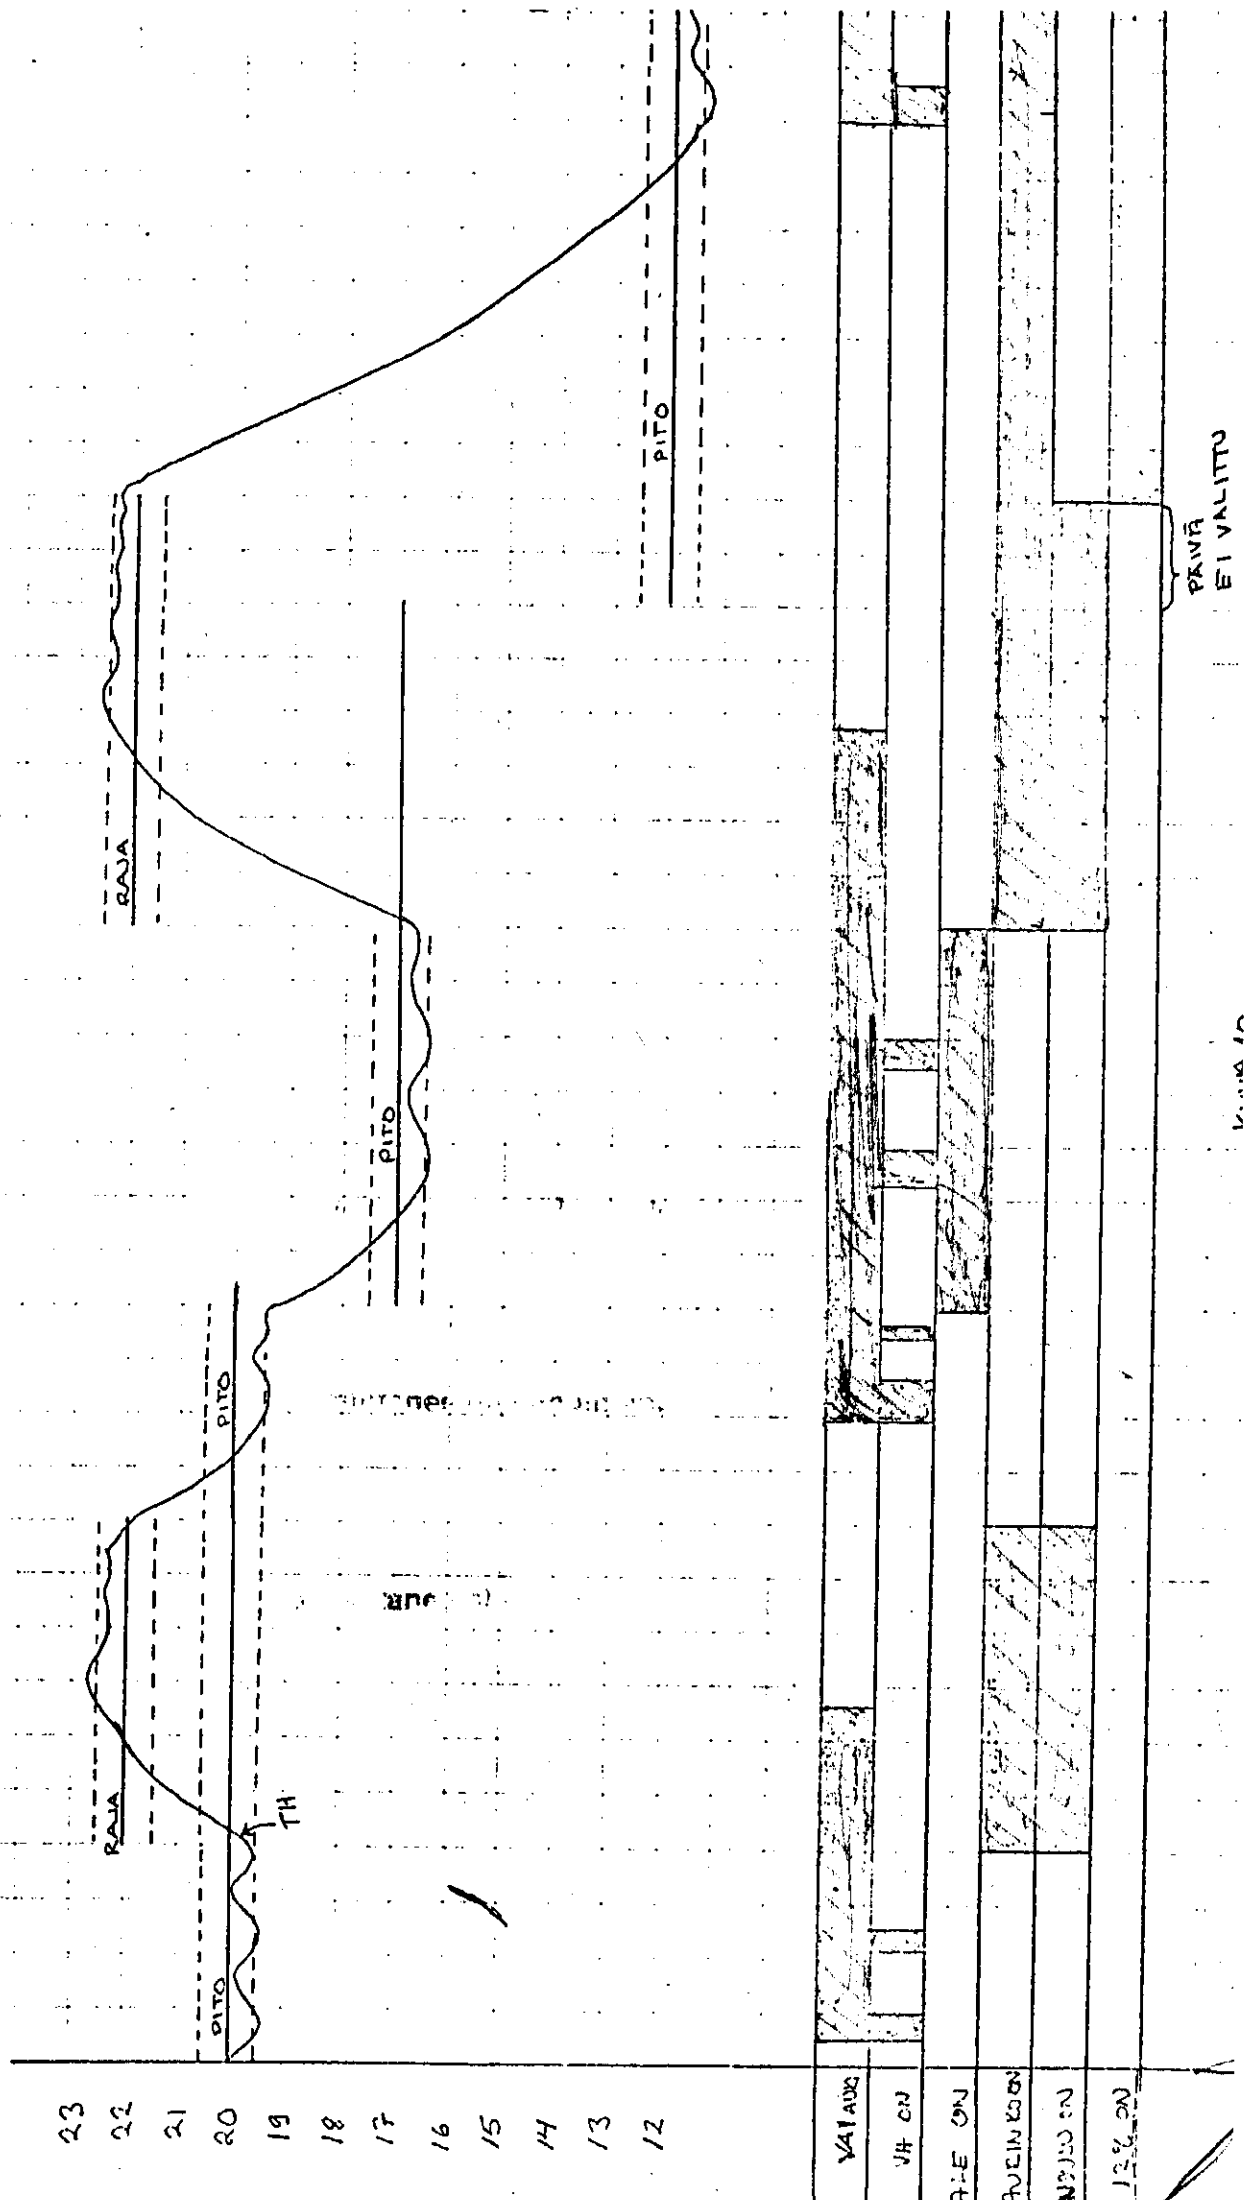



ESIMERKKI HUONEISTON LÄMPÖTILAN MUUTOKSISTA


$$A_H = 20^\circ\text{C}$$
$$\Delta H = 100$$
$$\Delta H = 20^\circ\text{C}$$


GHJELMAKAVIO

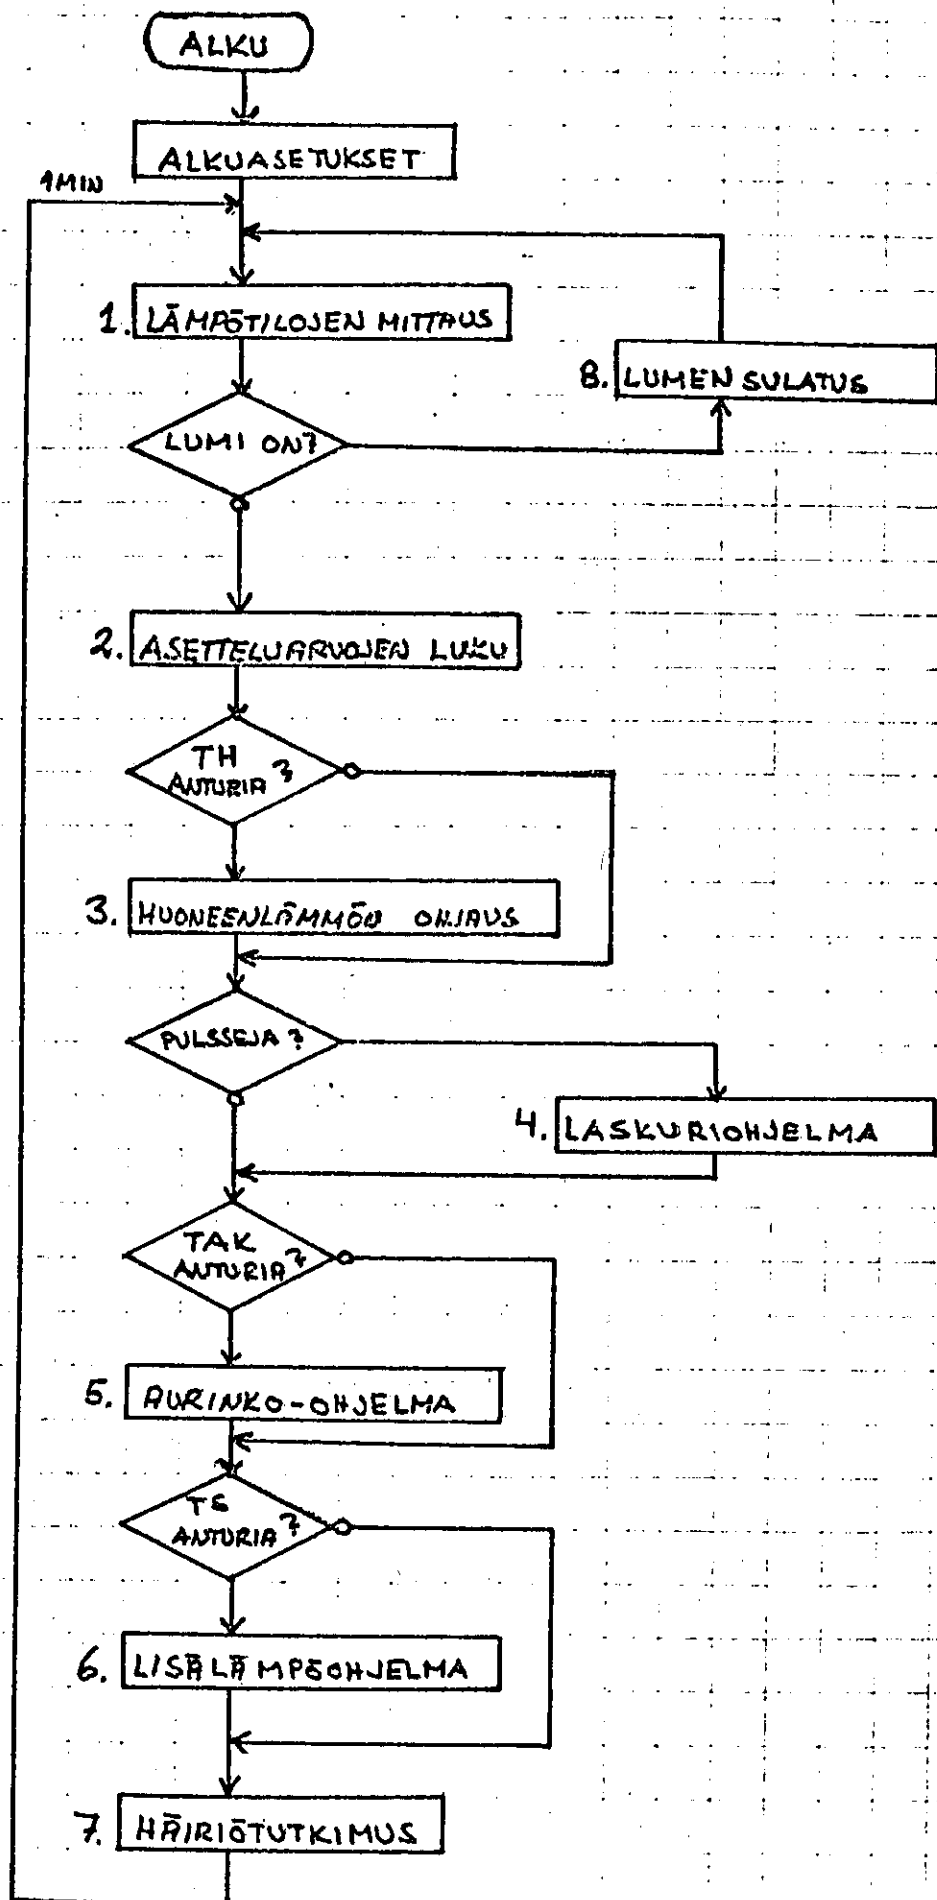


# 1. LÄMPÖTILASEN MITTAUS

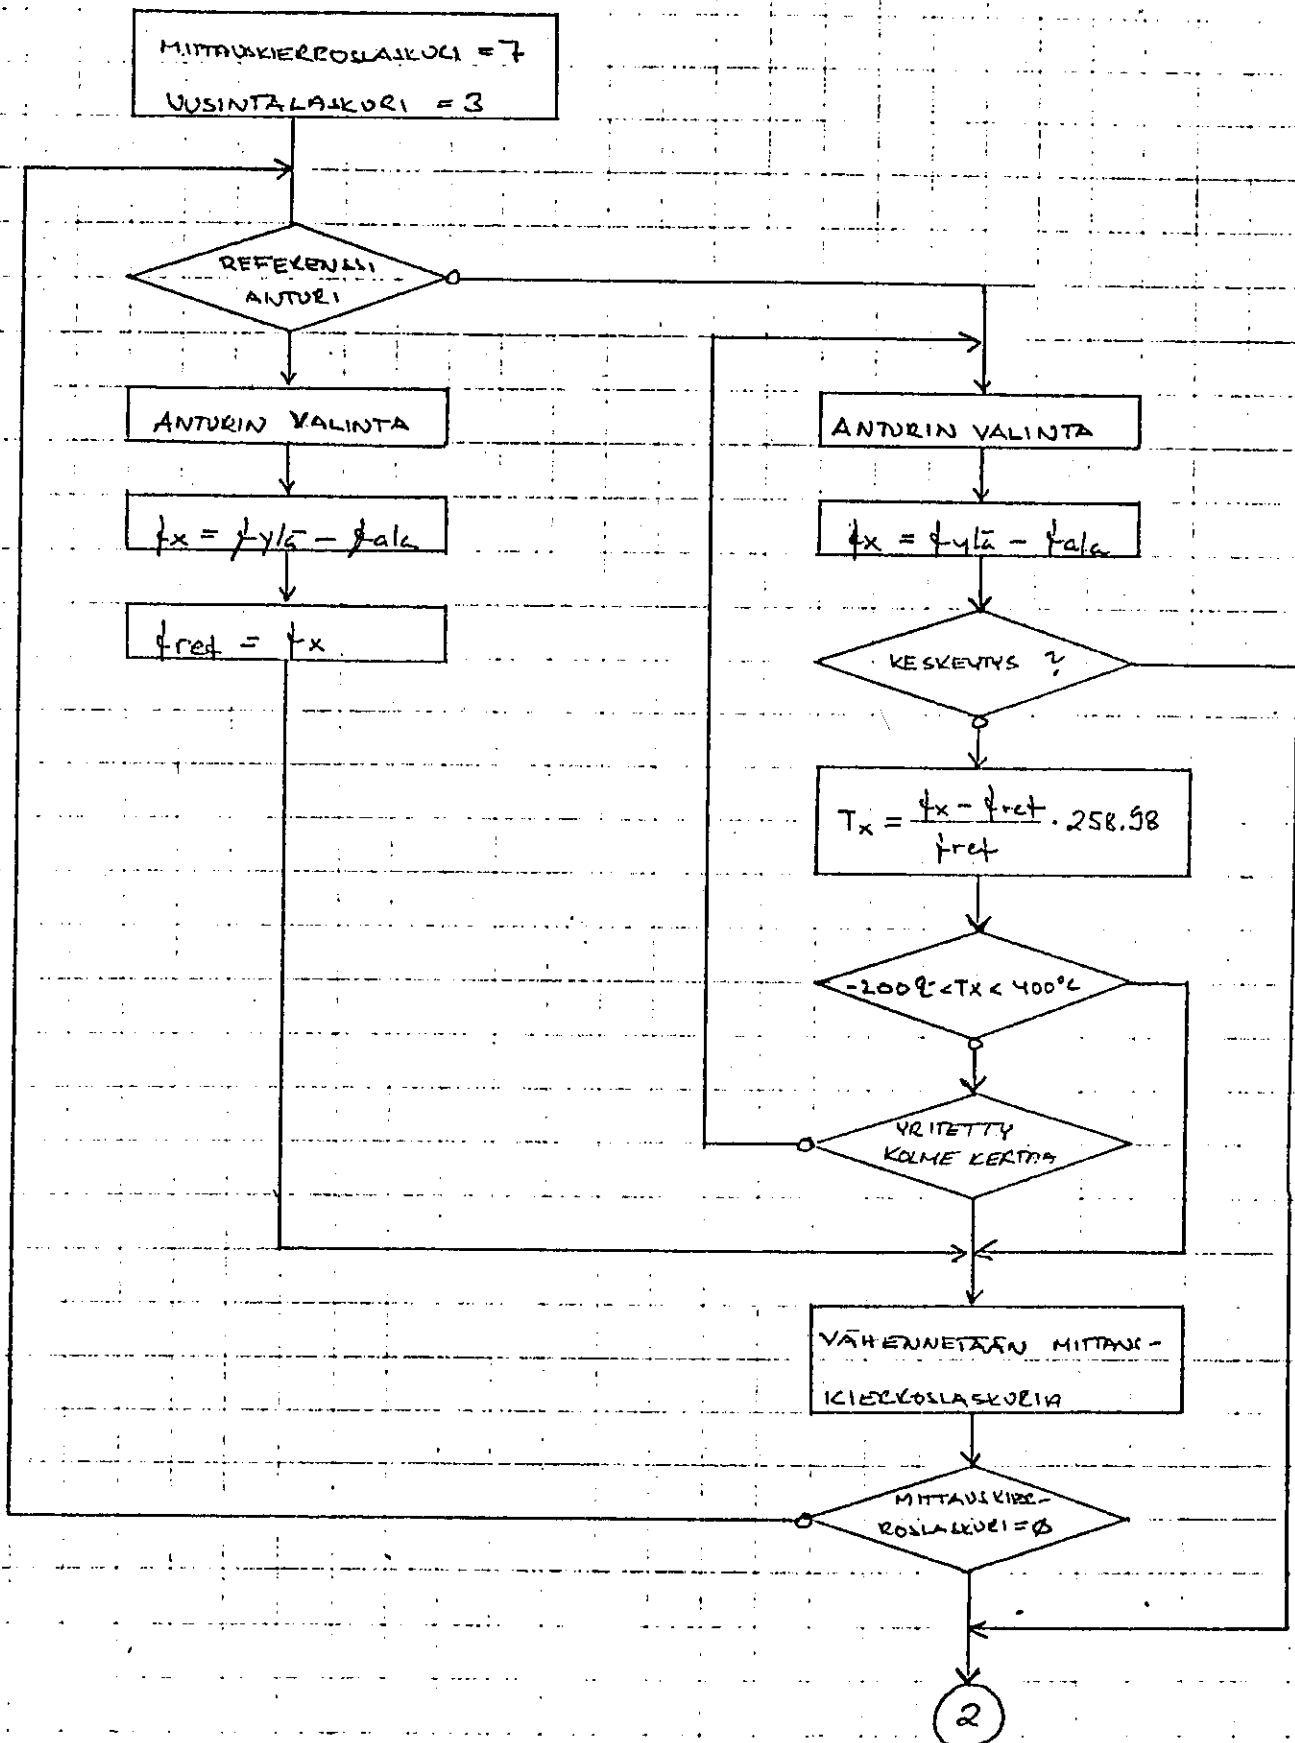

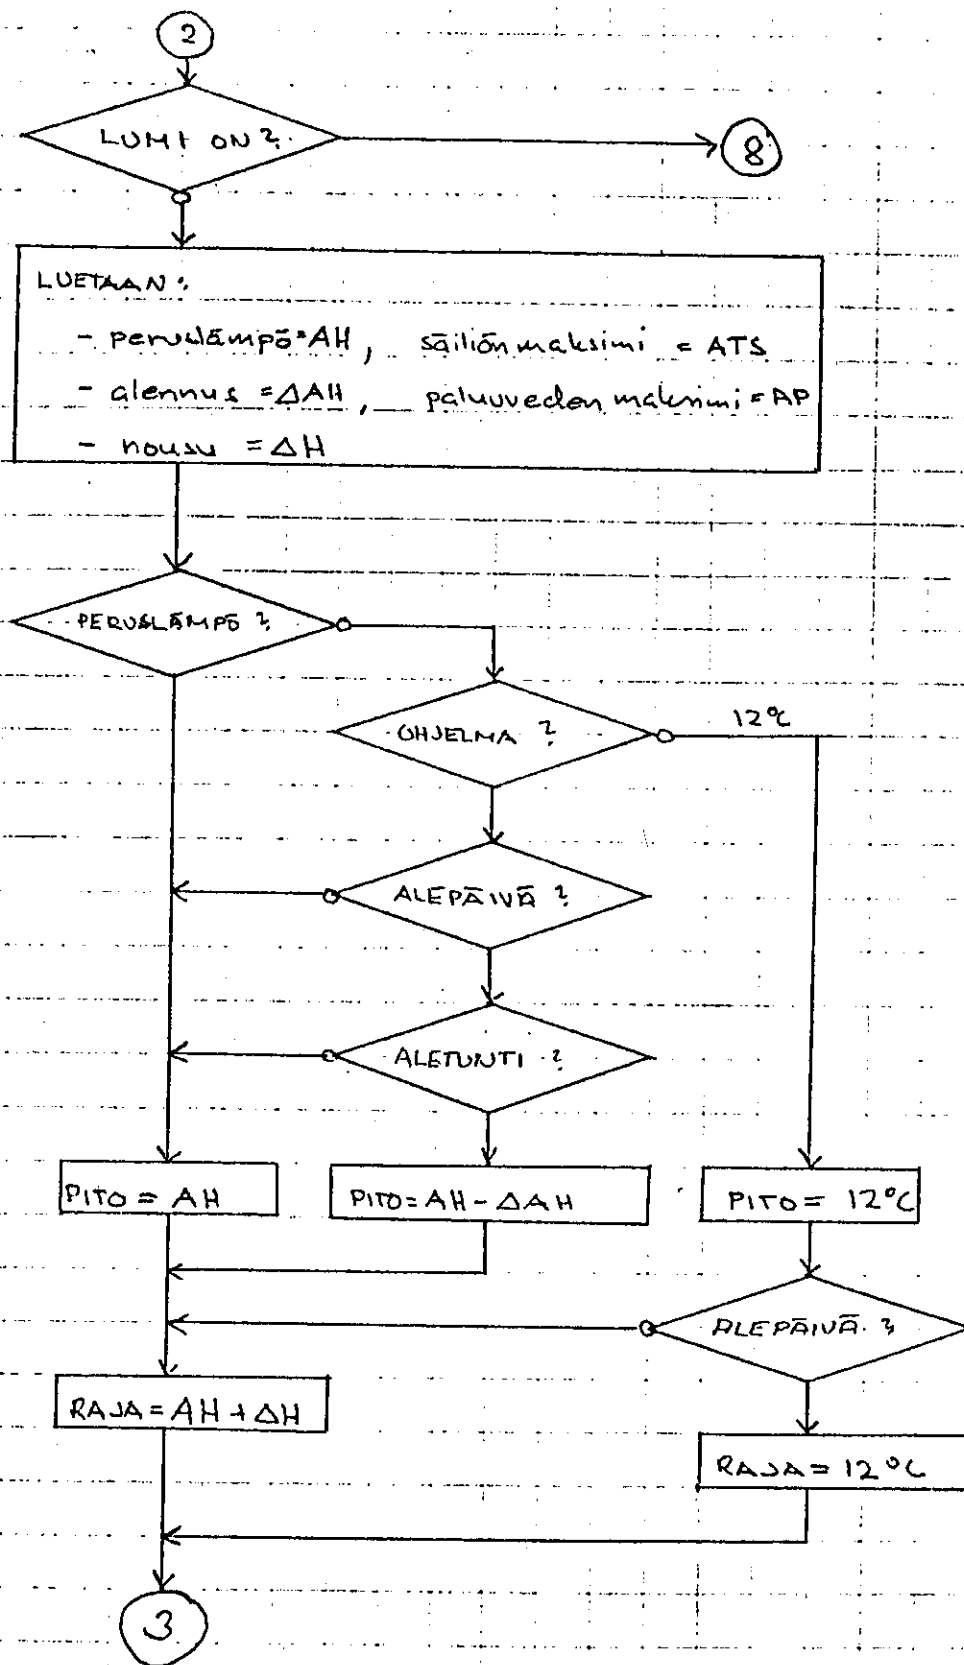


KUVA 9.2

### 3. HUONEENLÄMMÖN OHJOUS

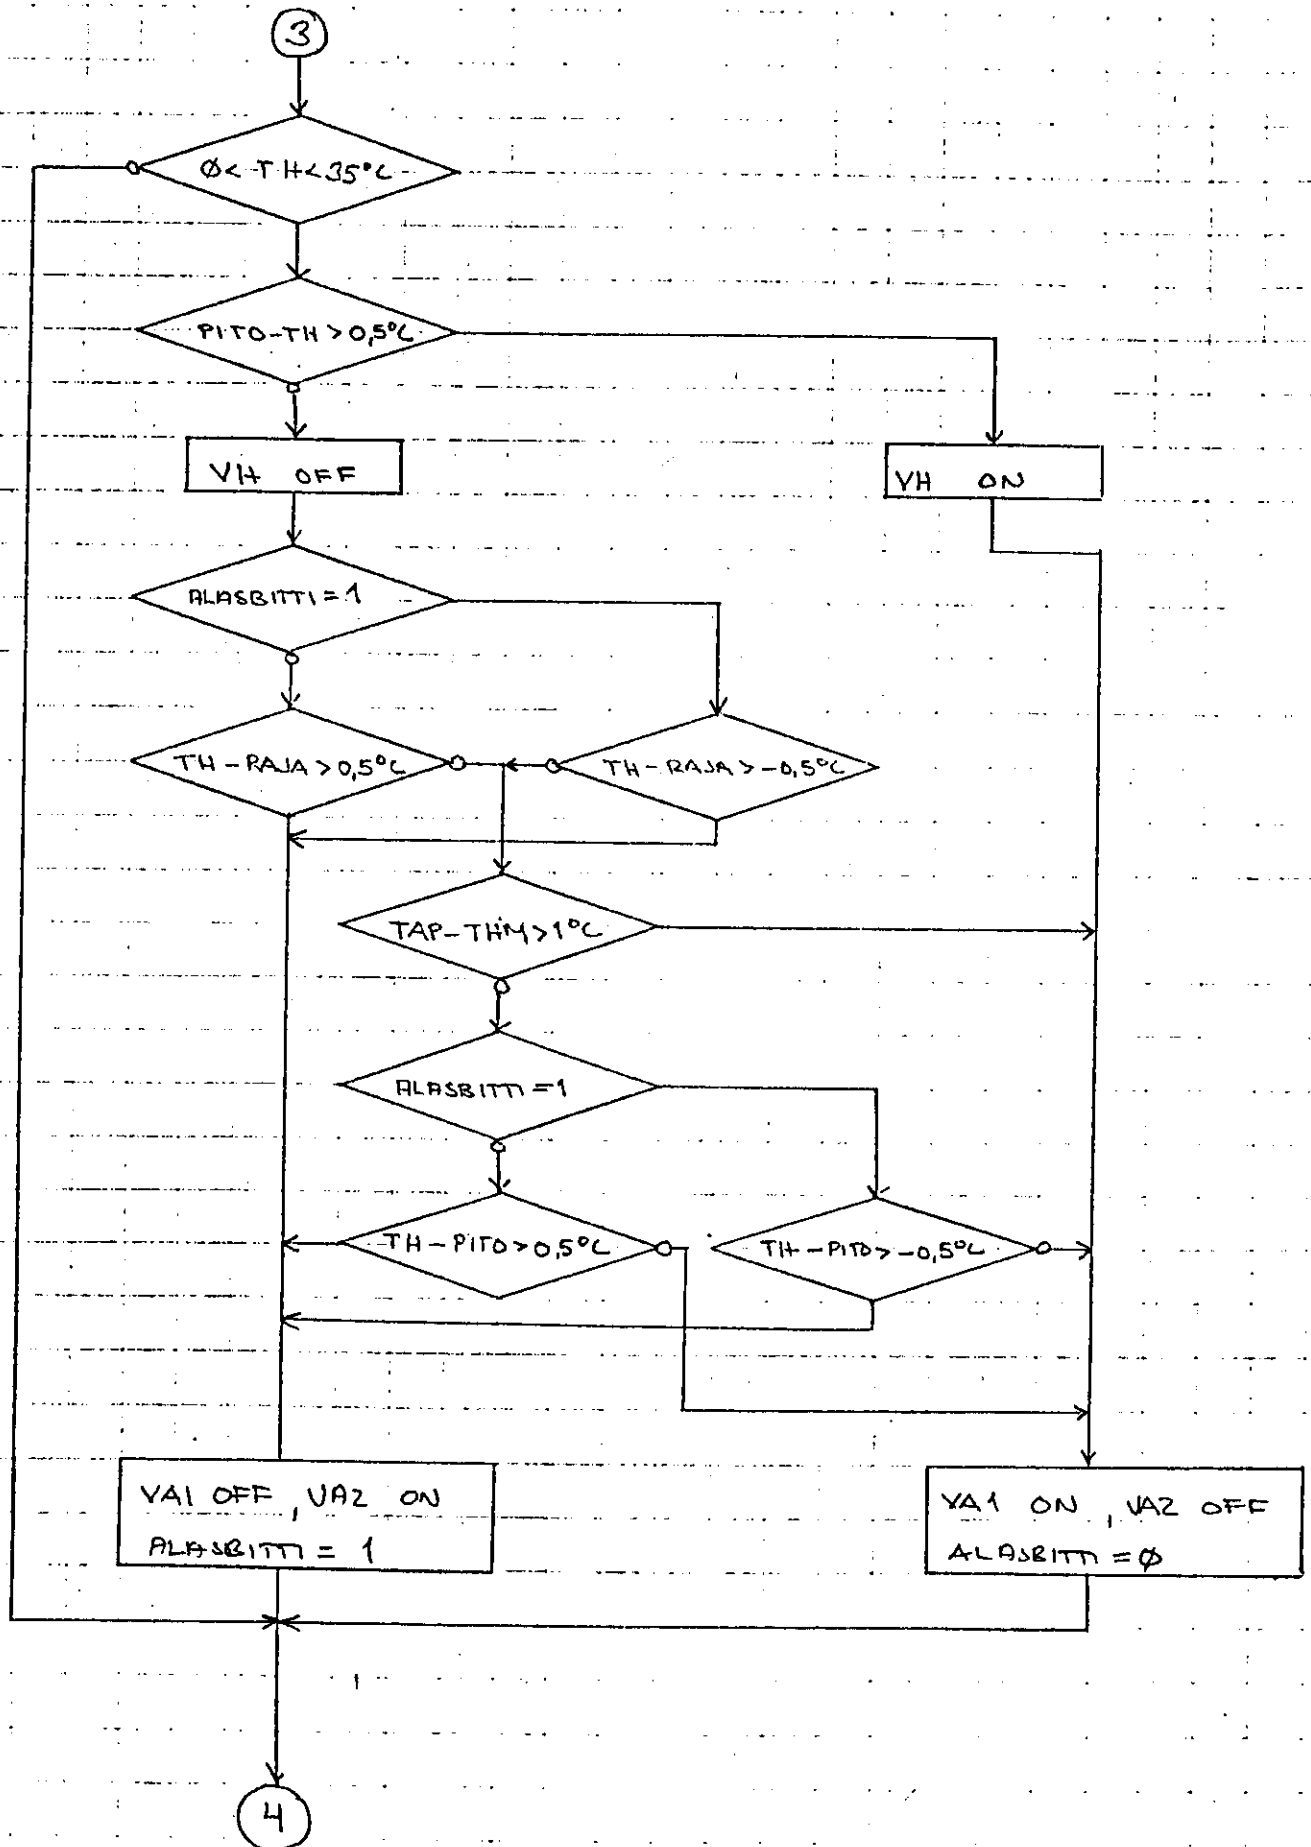


KUVA 5.3

#### 4. LASKURIOHJELMA

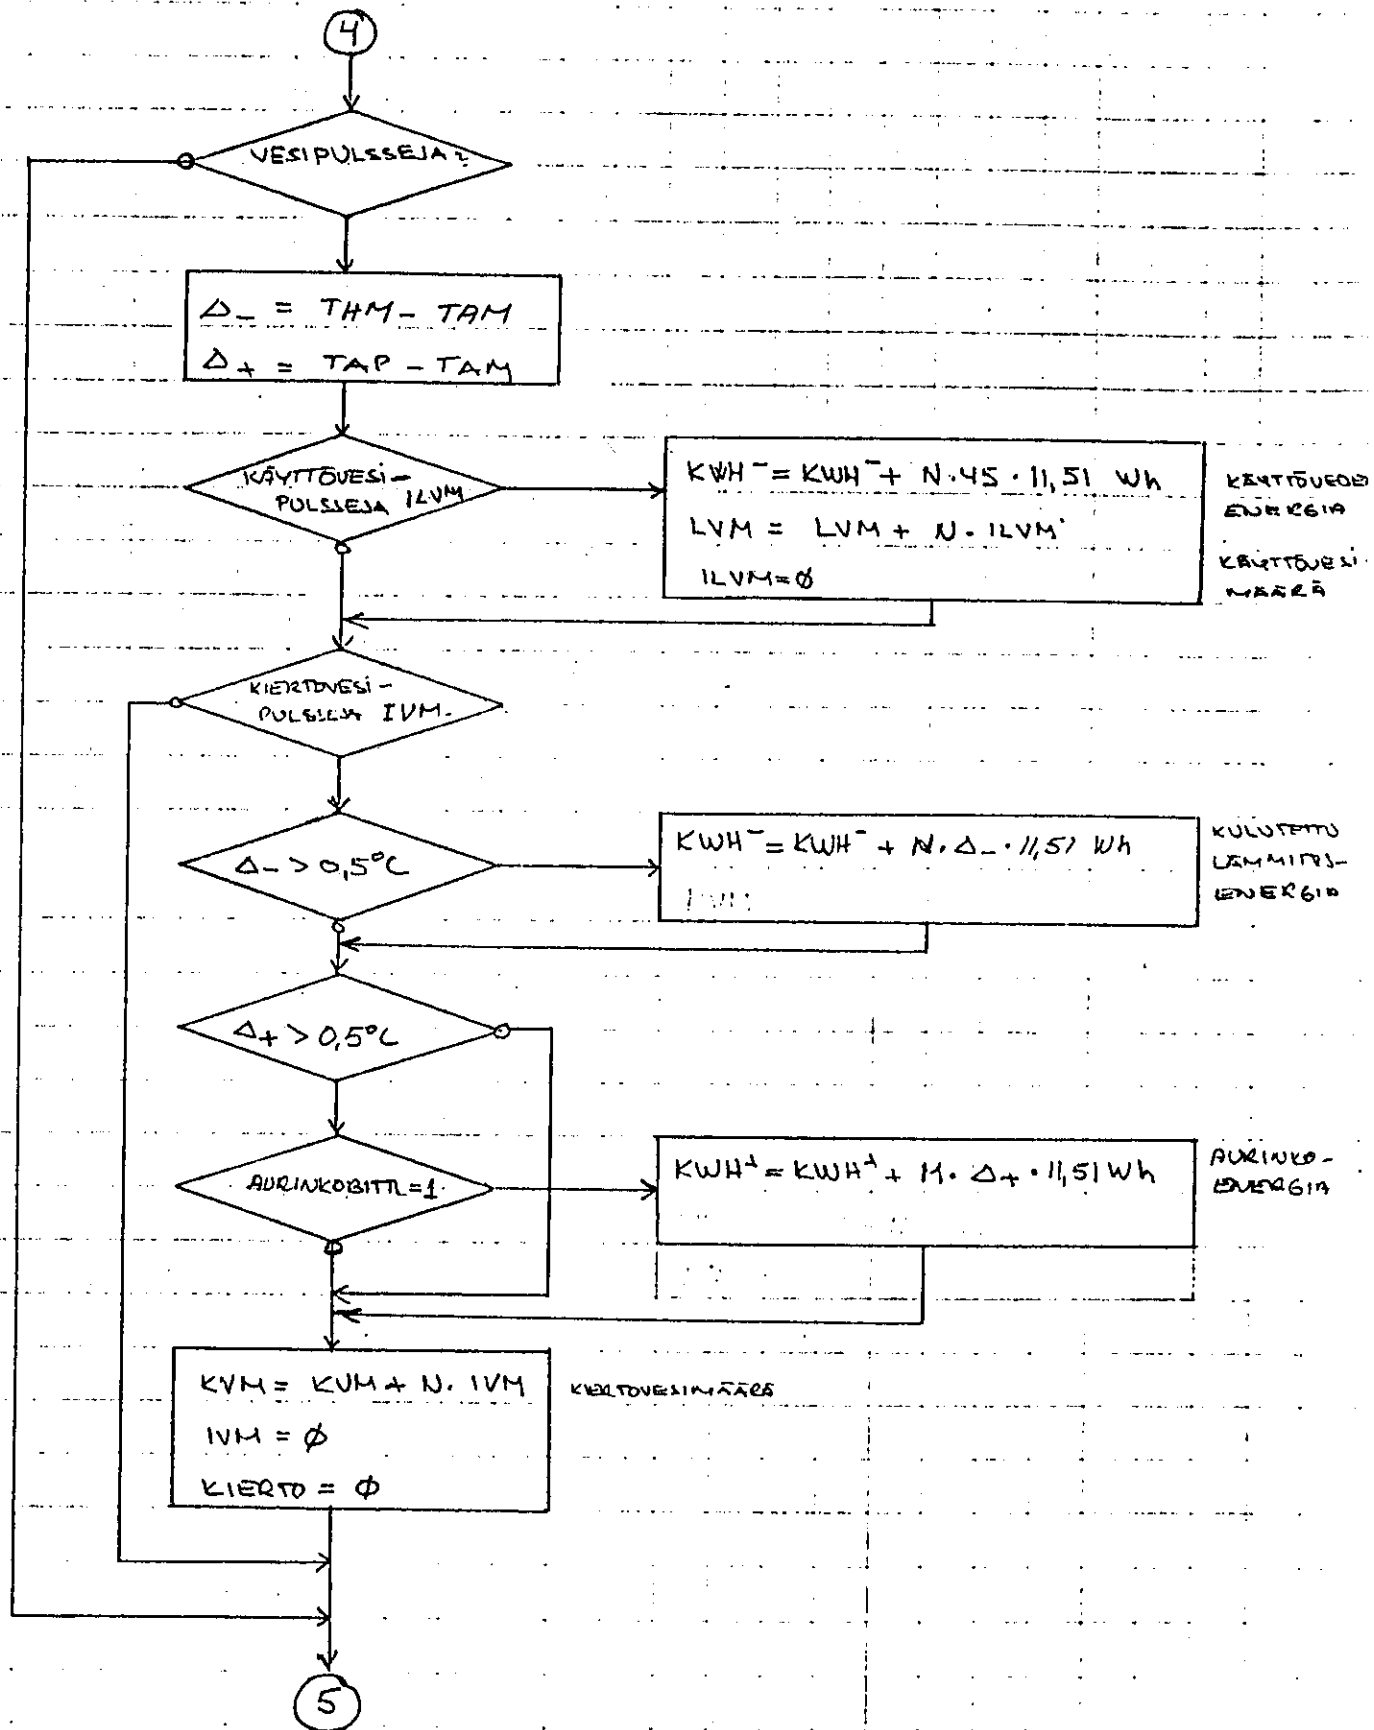


KUVA 9.4

# 5. AURINKO-OHJELMA

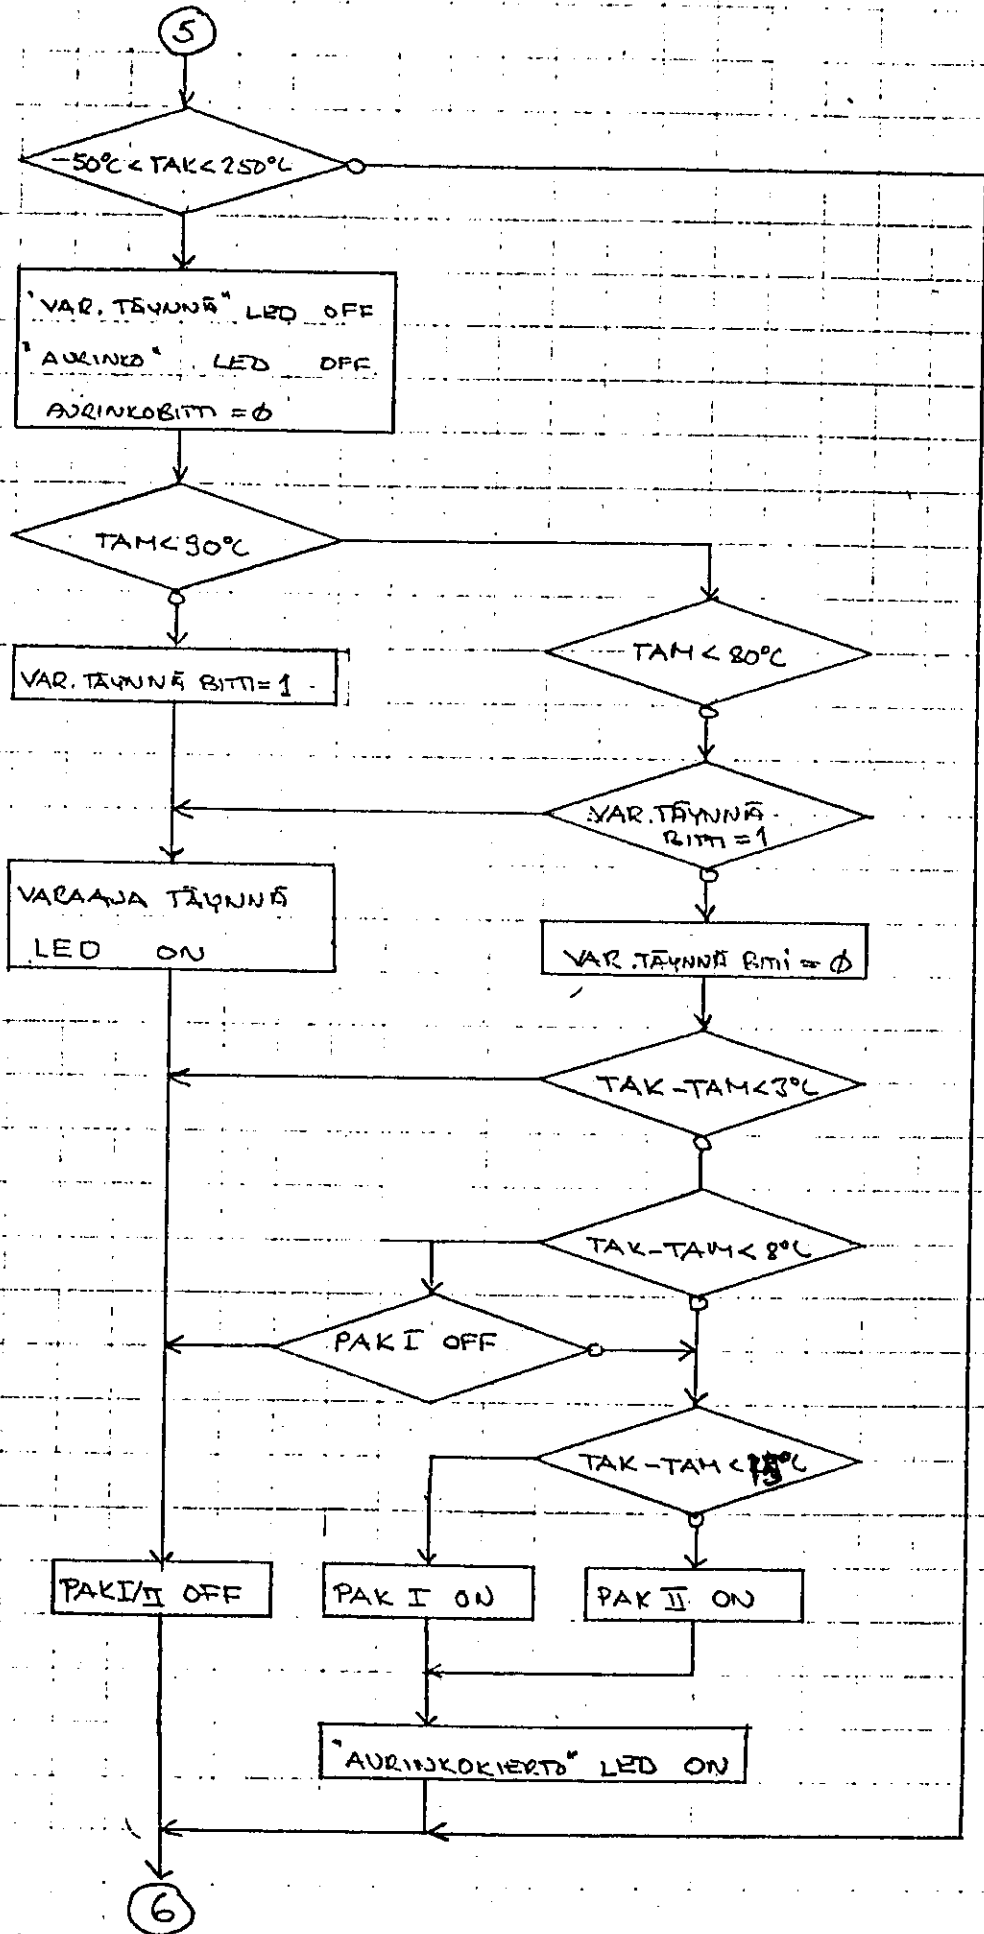


KUVA 9.5


# 6. LISPÄÄMPÖ OHJELMA

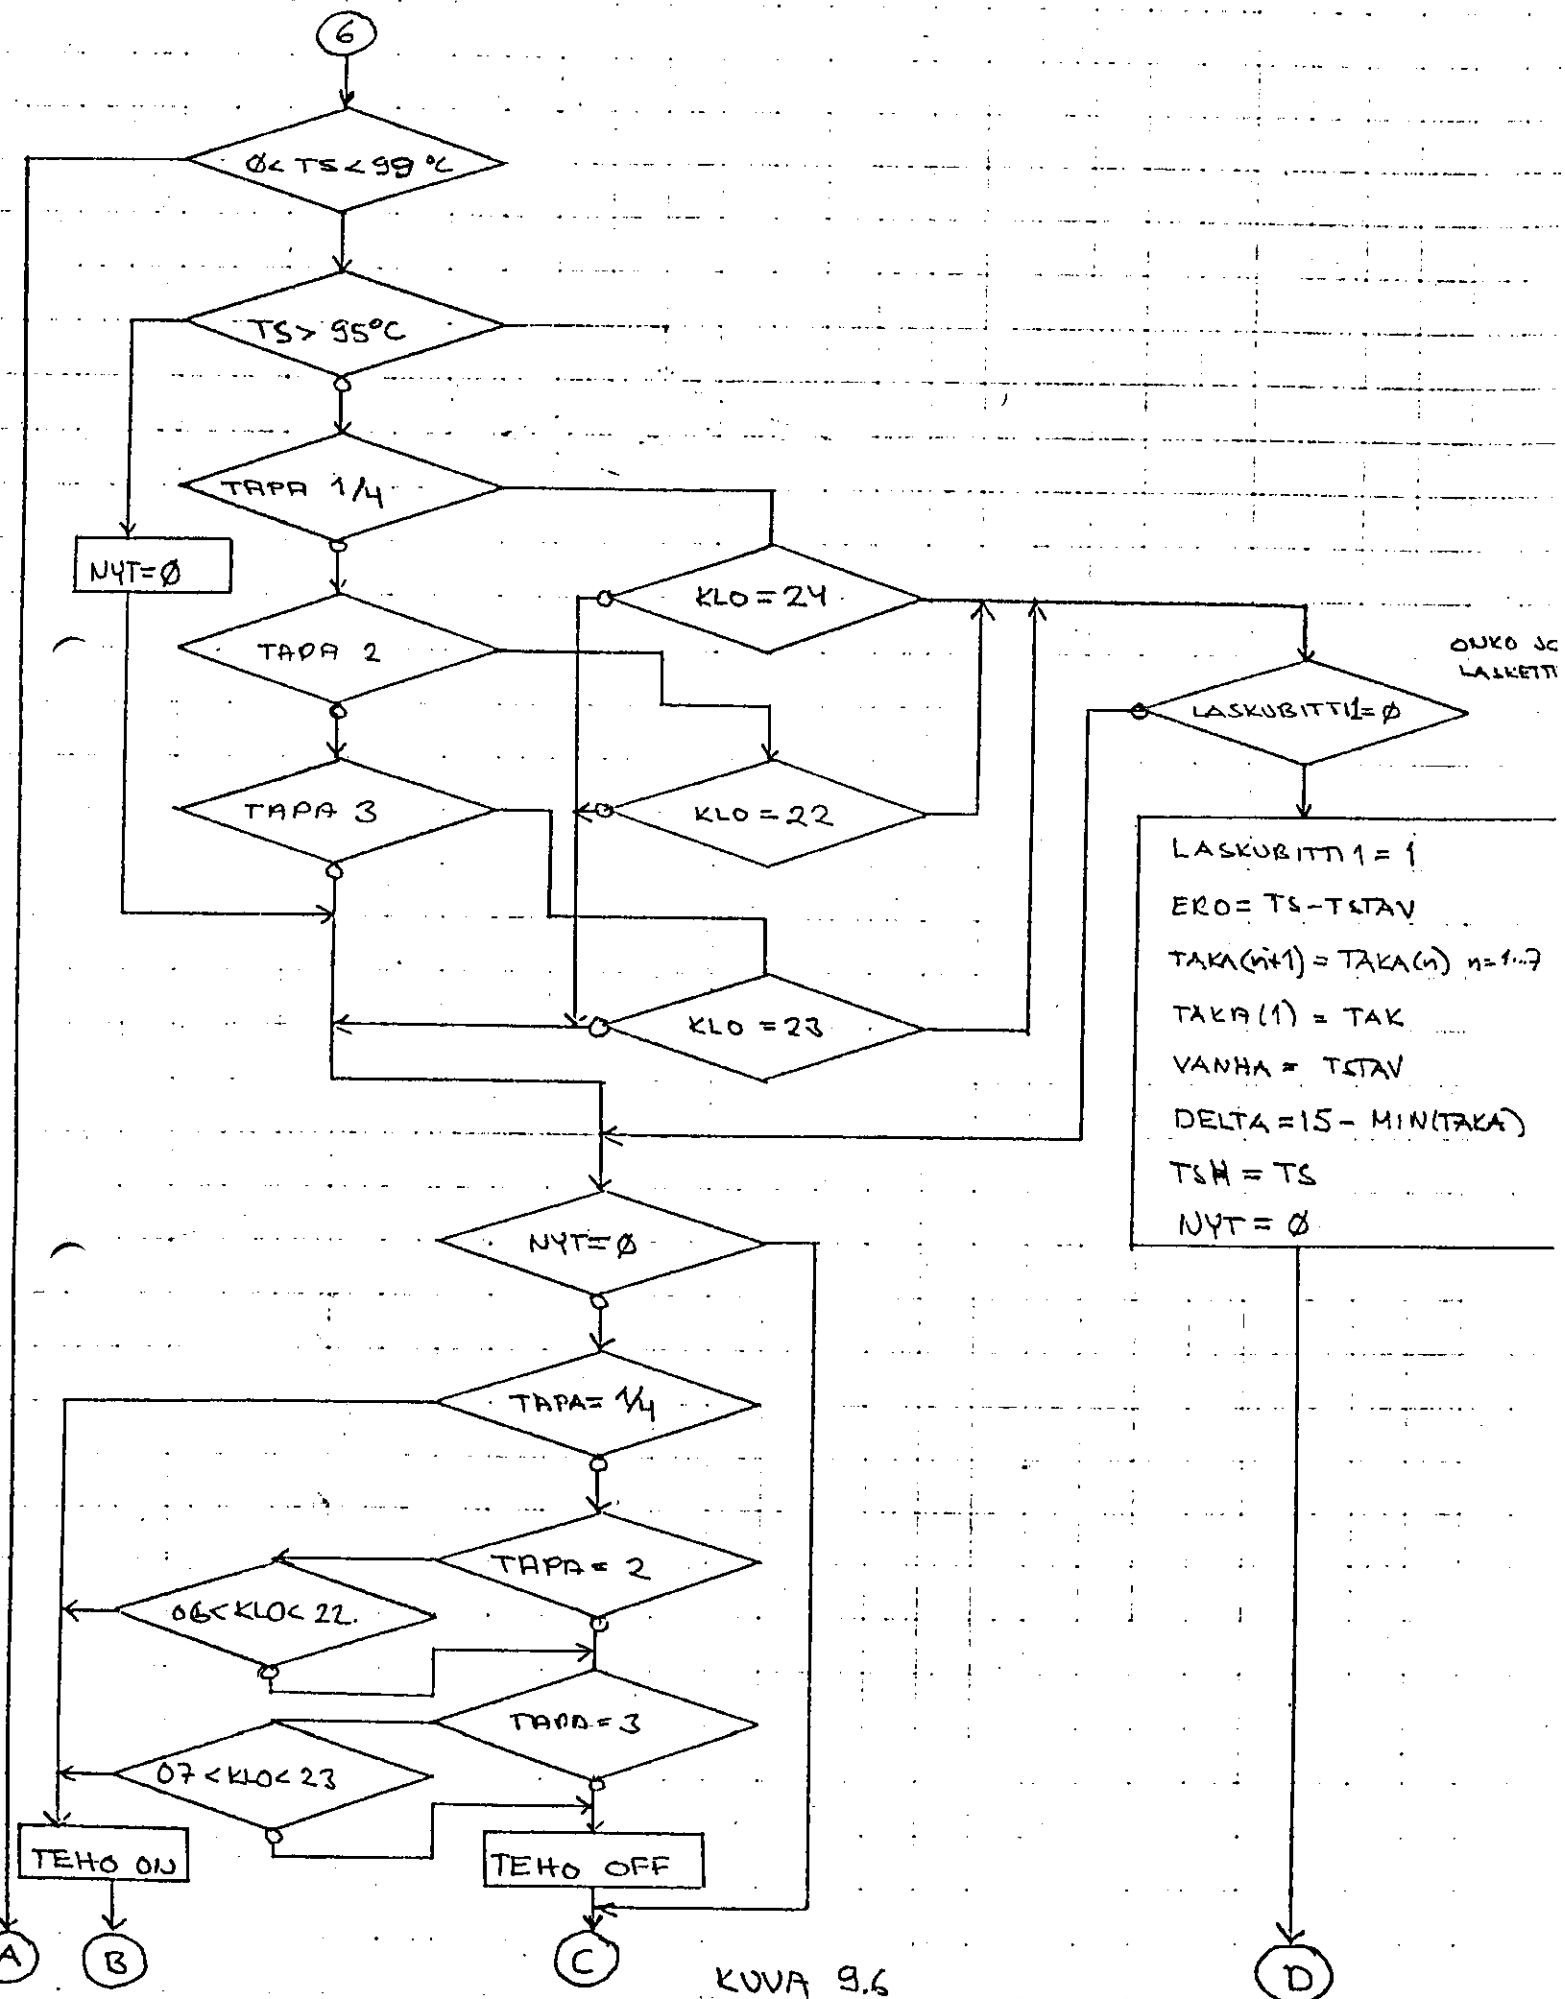



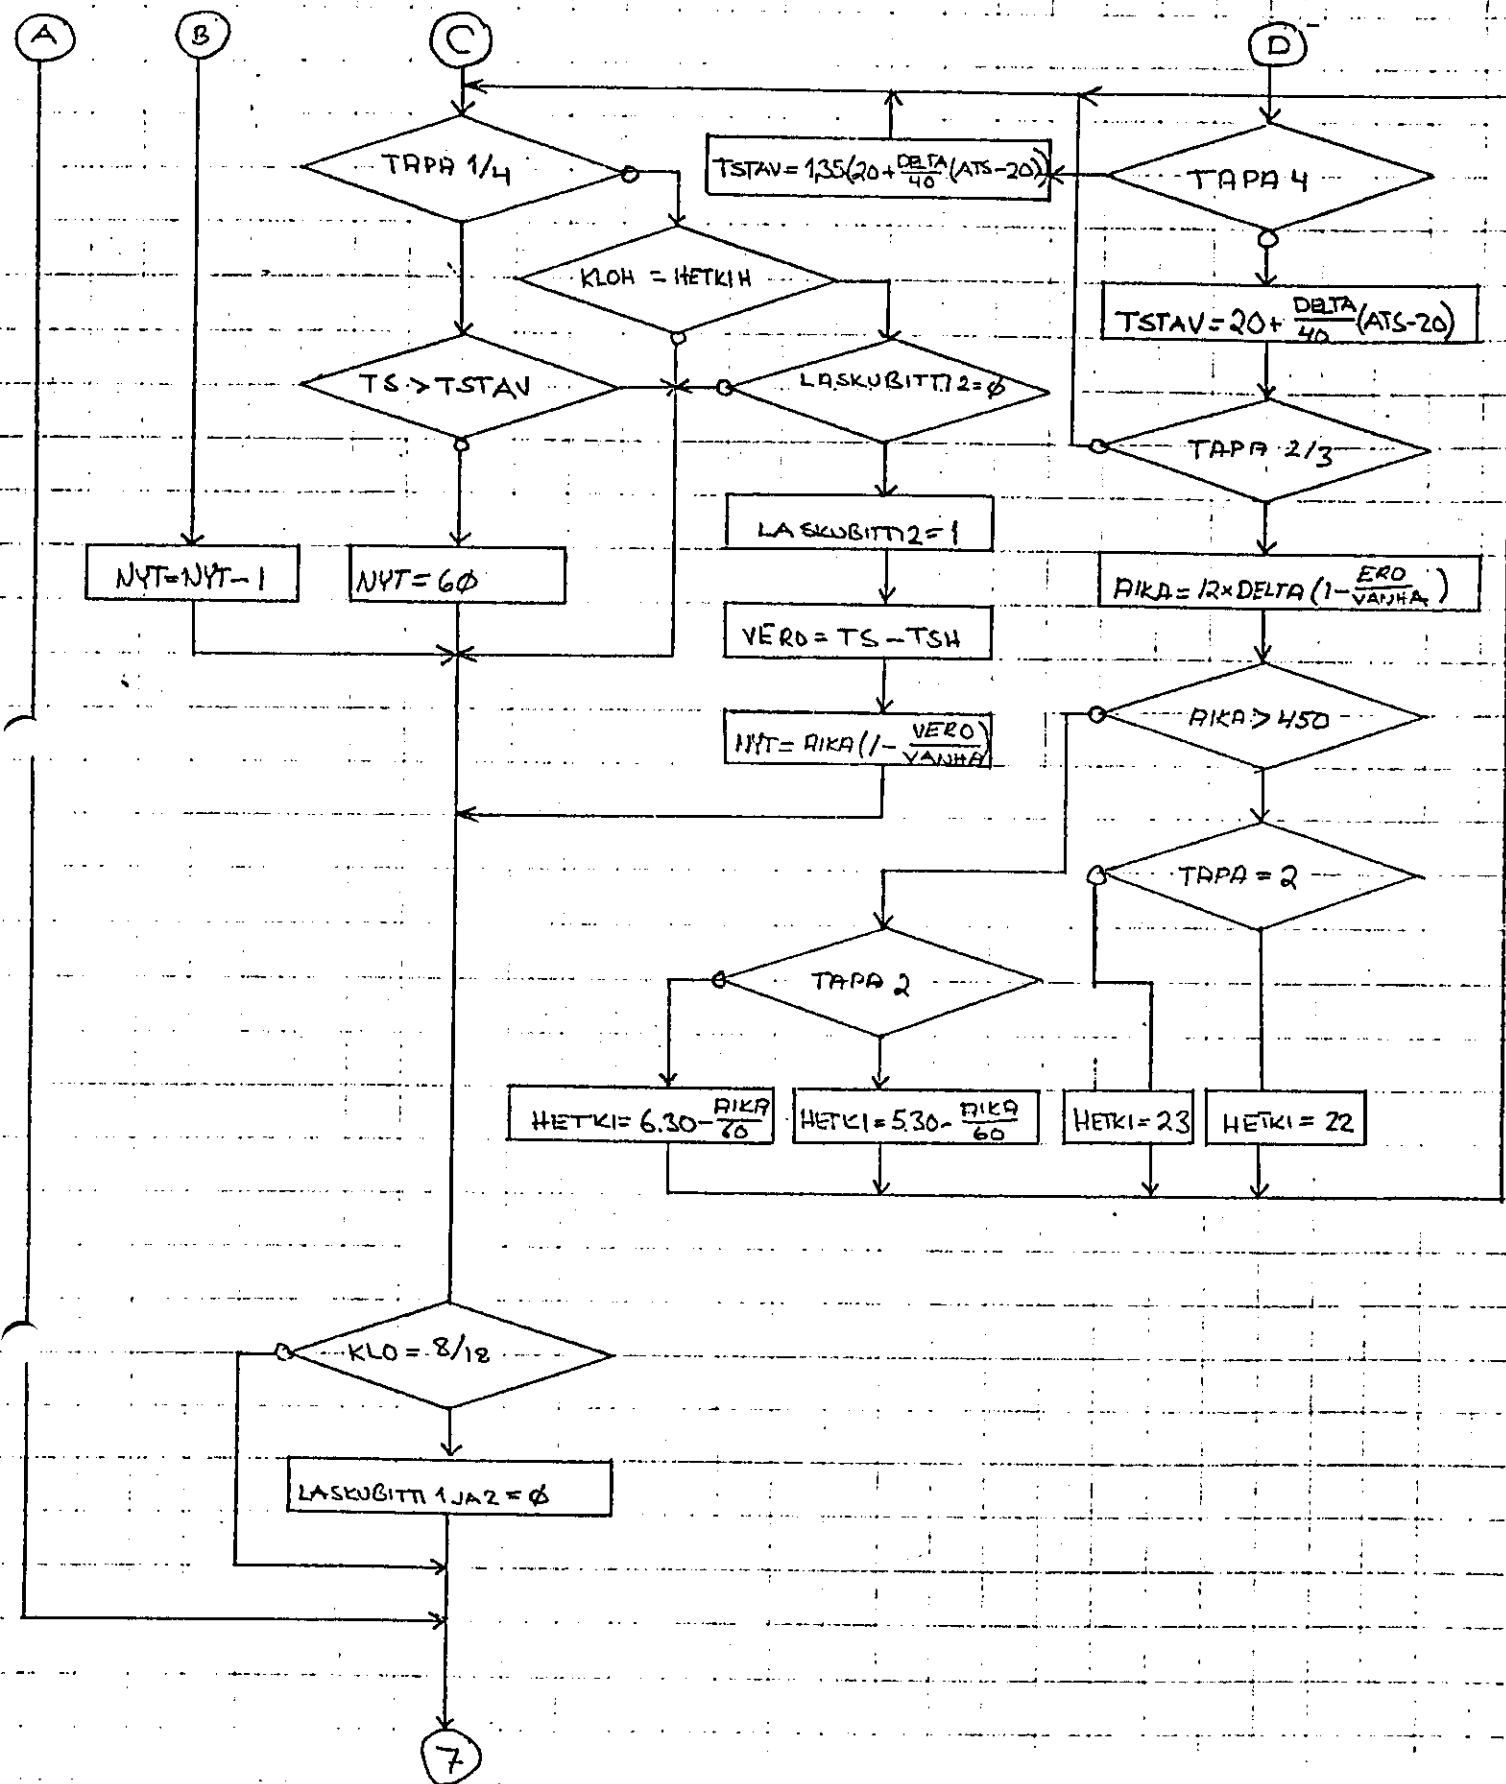


# 7. HÄIRIÖTUTKIMUS

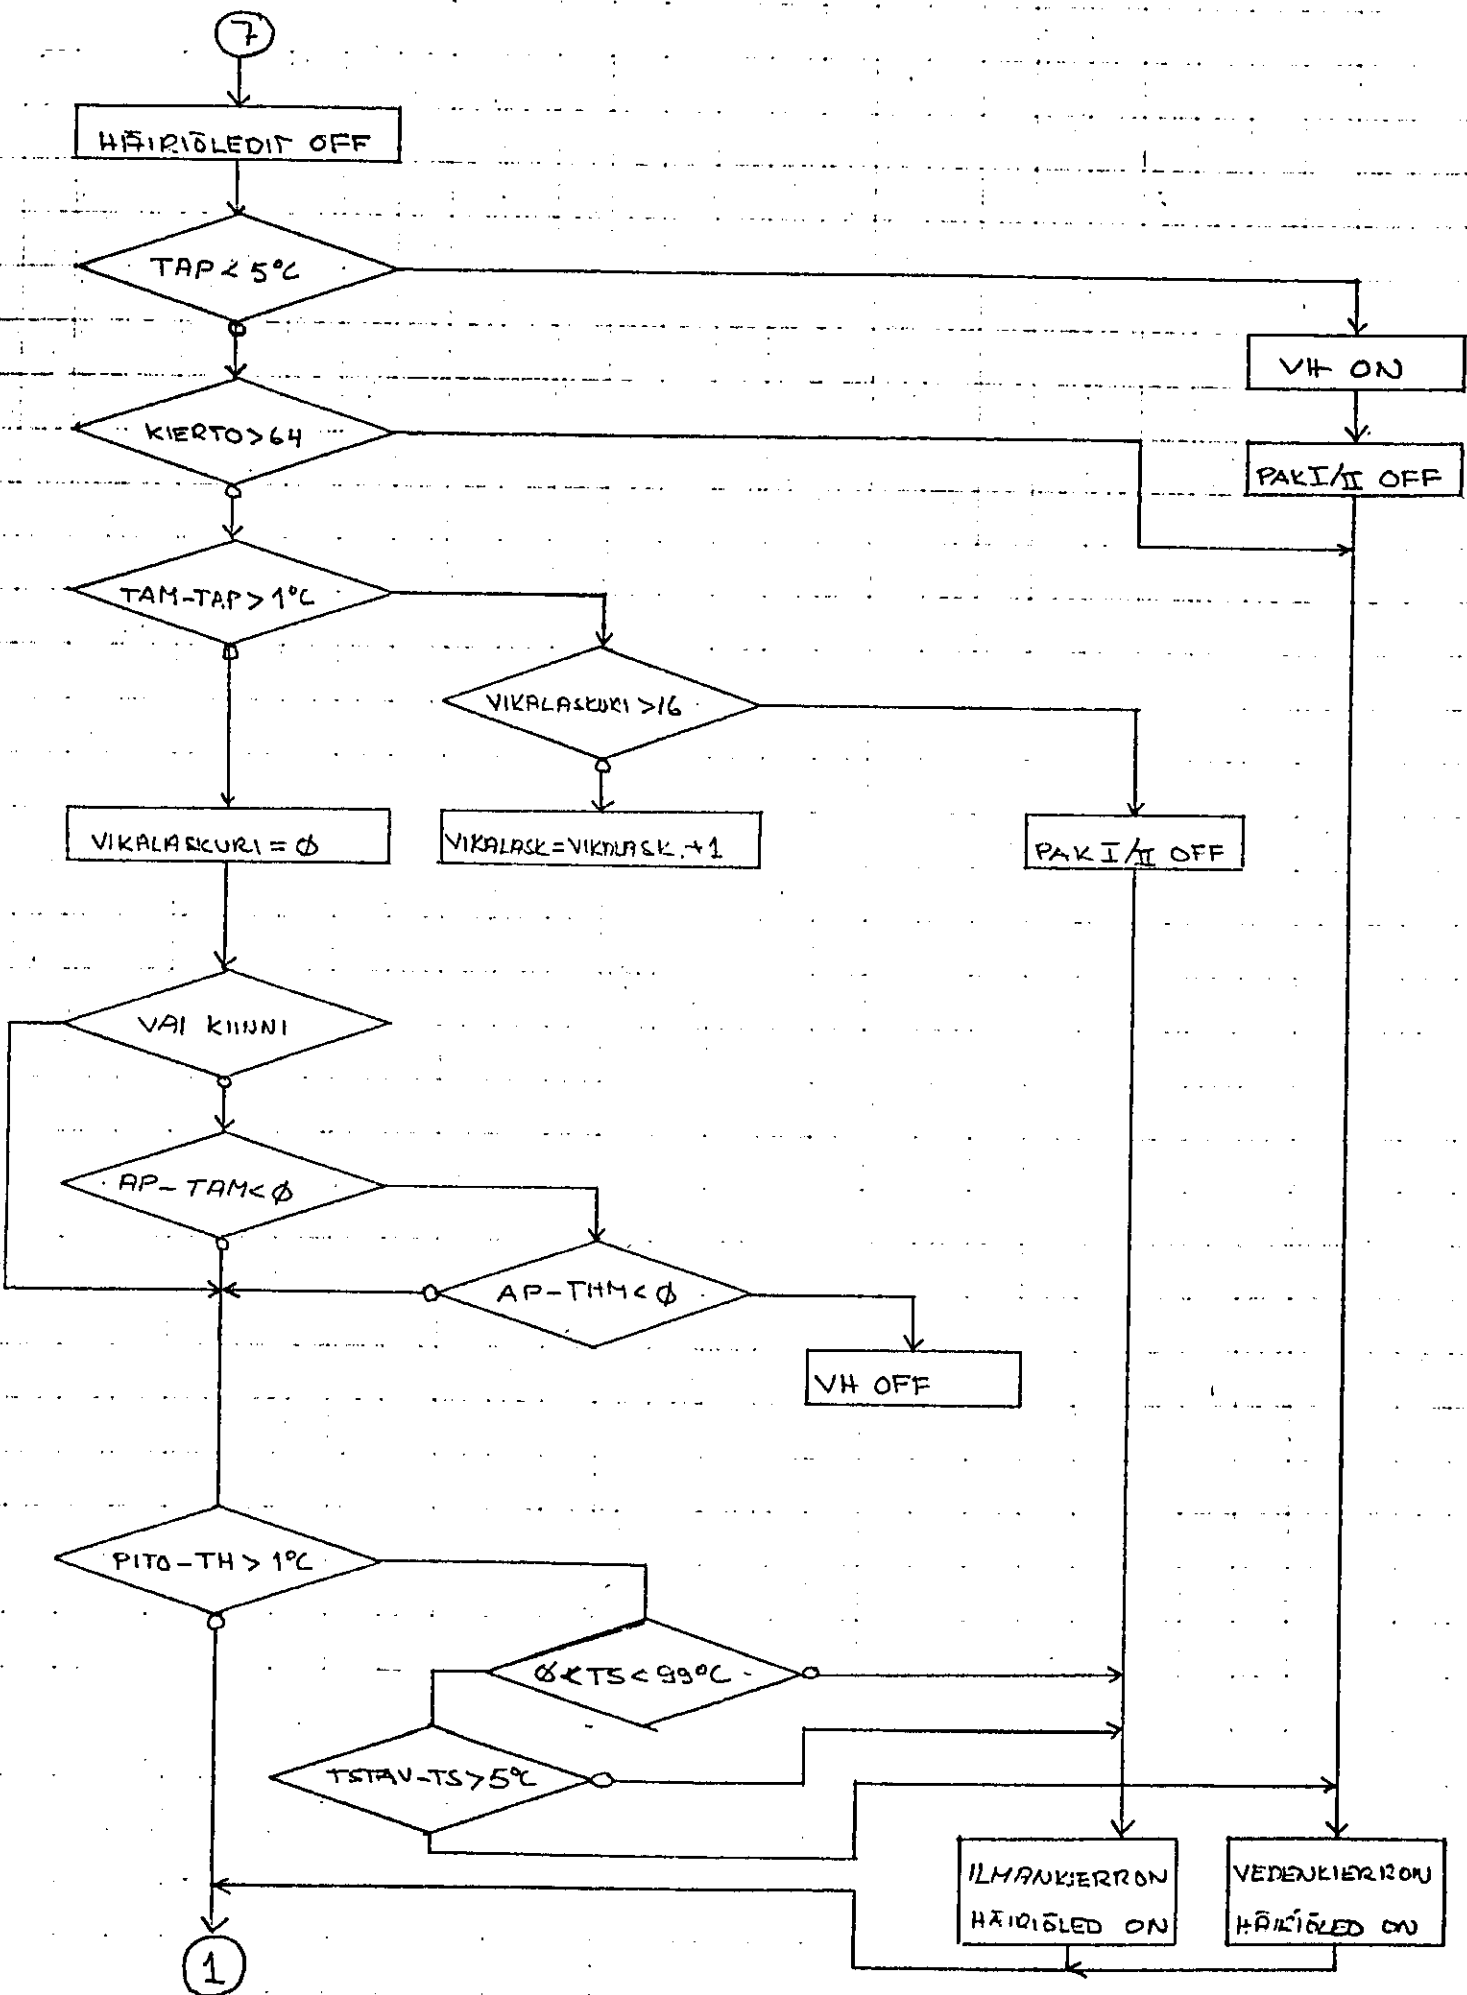


KUVA 9.7

### 8. LUMEN LULATUS

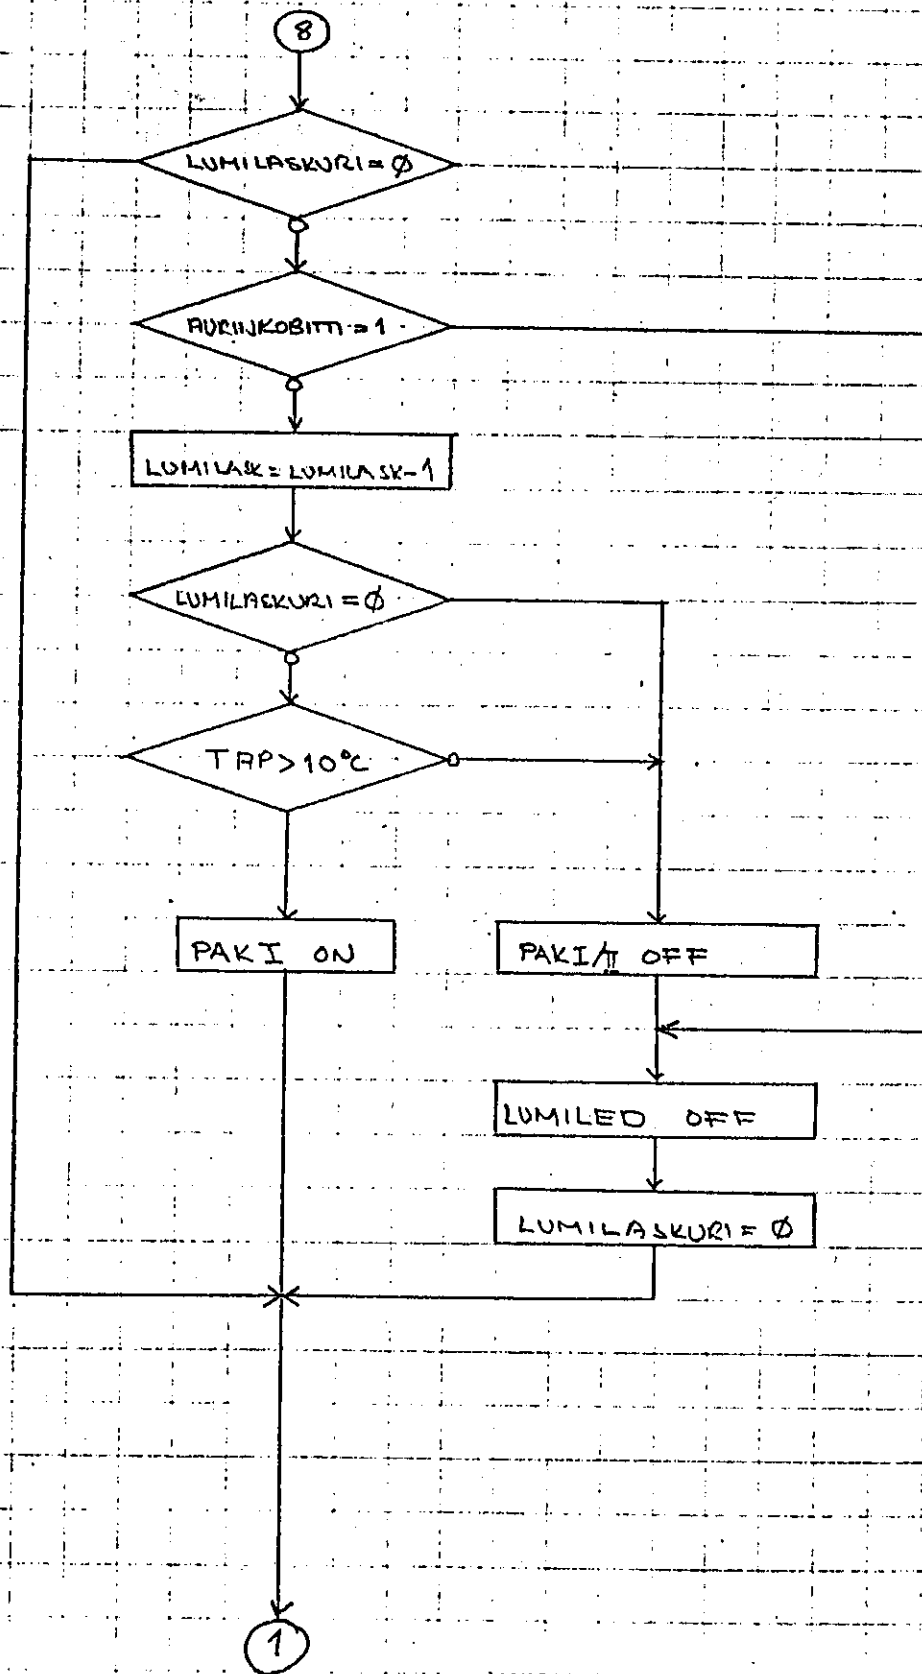


| Muutos kirjain | Esitelly kert.n:o | Muutoksen kuvaus | Muutosehdotuksen n:o | Pvm | Muuttanut | Tark. |
|----------------|-------------------|------------------|----------------------|-----|-----------|-------|
|                |                   |                  |                      |     |           |       |

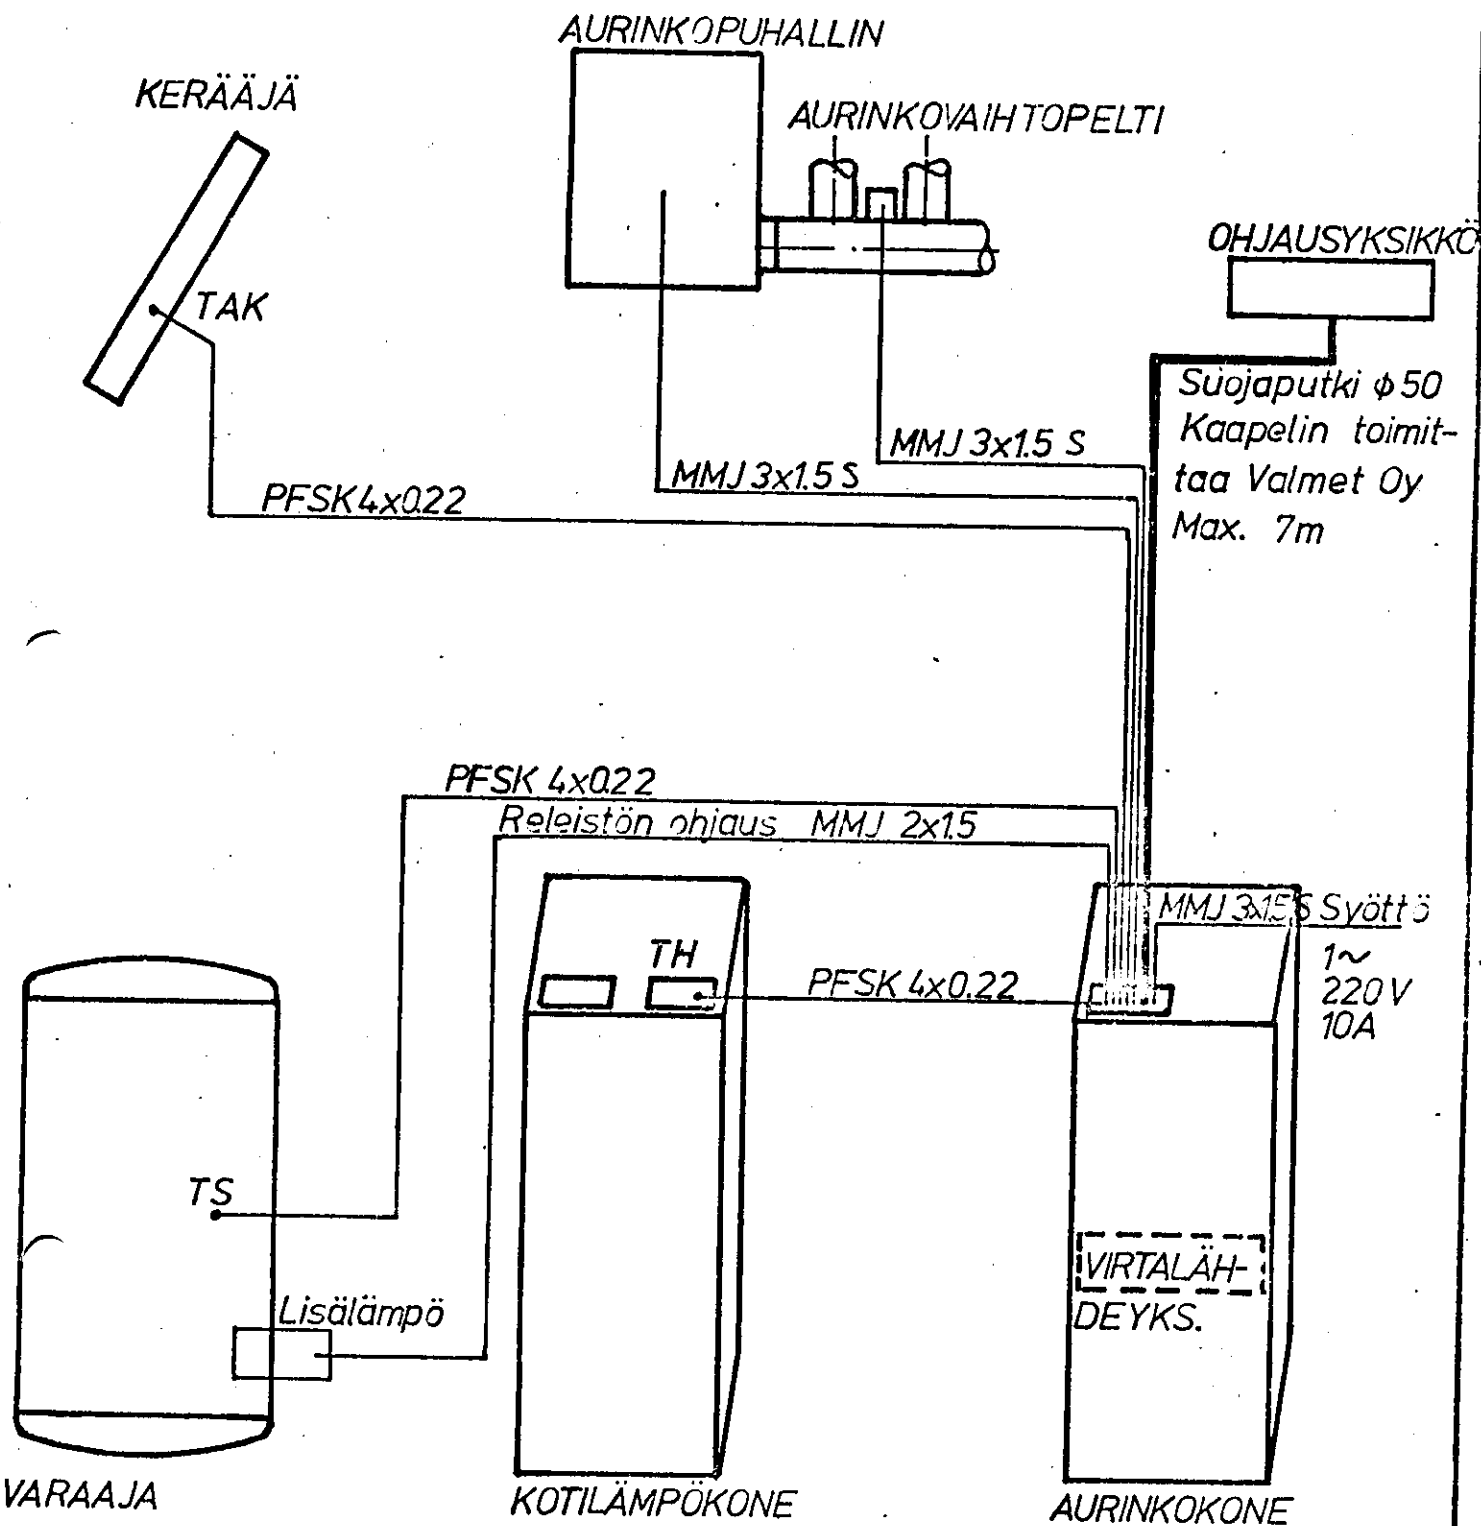

|                                       |           |                                 |                            |              |        |                 |                 |      |  |
|---------------------------------------|-----------|---------------------------------|----------------------------|--------------|--------|-----------------|-----------------|------|--|
|                                       |           |                                 |                            |              |        |                 |                 |      |  |
| Piirustus n:o<br>Tavaratunnus         |           | Nimitys/Rakenneaine             |                            |              |        | Tarve/kokop.    |                 | Yks. |  |
| 1980-07-17                            | <i>TH</i> | Pintamerkit:<br>SFS 2039        | Toleranssit:<br>A SFS 3393 | Projisointi: | Suhde: | Laskettu:<br>kg | Punnittu:<br>kg |      |  |
|                                       |           | Ra<br>▽                         | Ra hiottu<br>▽             |              |        | Ent.            |                 |      |  |
|                                       |           | Valmiste:                       |                            |              |        | Liittyy:        |                 |      |  |
| <b>AURINKOKONEEN</b><br>ANSION TEHDAS |           | AURINKOKONEEN ULKOINEN JOHDOTUS |                            |              |        | KUVA 6          |                 |      |  |

# LYHENTEET

TH=huoneenlämmön anturi  
 TAK=aurinkokerääjän anturi  
 THM=lämmityksen menoveden anturi  
 TAM=aurinkolämpönsäätimen menoveden anturi  
 TAP= " " paluuveden anturi  
 TS=varaajasilin anturi  
 VM=lämmityksen kiertovesimäärän anturi  
 LVM=lämpimän käyttöveden anturi  
 VA1,VA2=magneettiventtiilejä  
 VP=kiertovesipumppu  
 VH=kolmitieventtiili  
 PM1,PM2=peittimoottorit  
 PK=pääkytkin  
 VPK=vesipumpun kytkin  
 PAK=aurinkopuhaltimen kytk.  
 AE=aurinkoenergia  
 LE=kulutettu energia  
 pulssit kaukonäyttöön

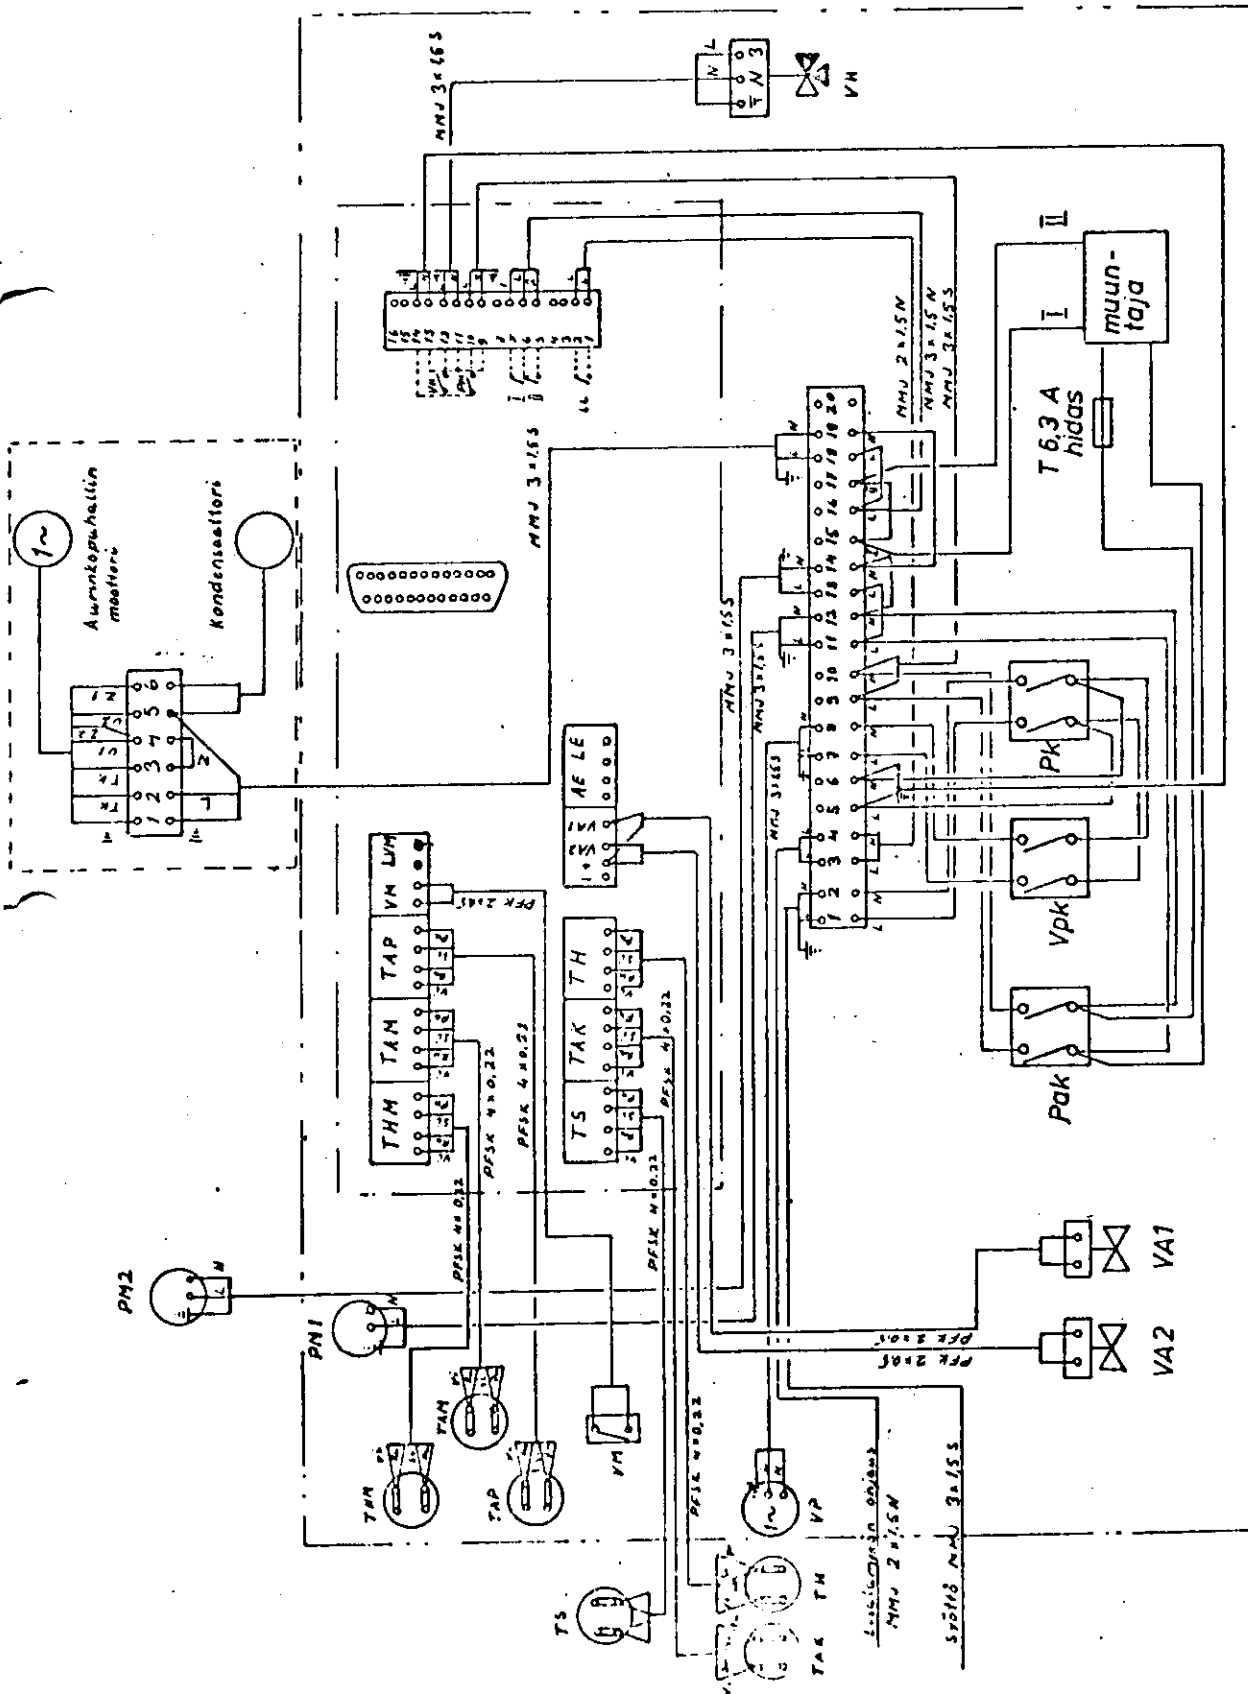

Huom. Anturikaapelin metallisuutta taitetaan liittopuolella vedonpoistajan alle ja jätetään anturipuolella liittämättä.

Jos käytetään piirturia ja pariantureita on kytkentä seur.

